



GF180 Tapeout - Floorplan

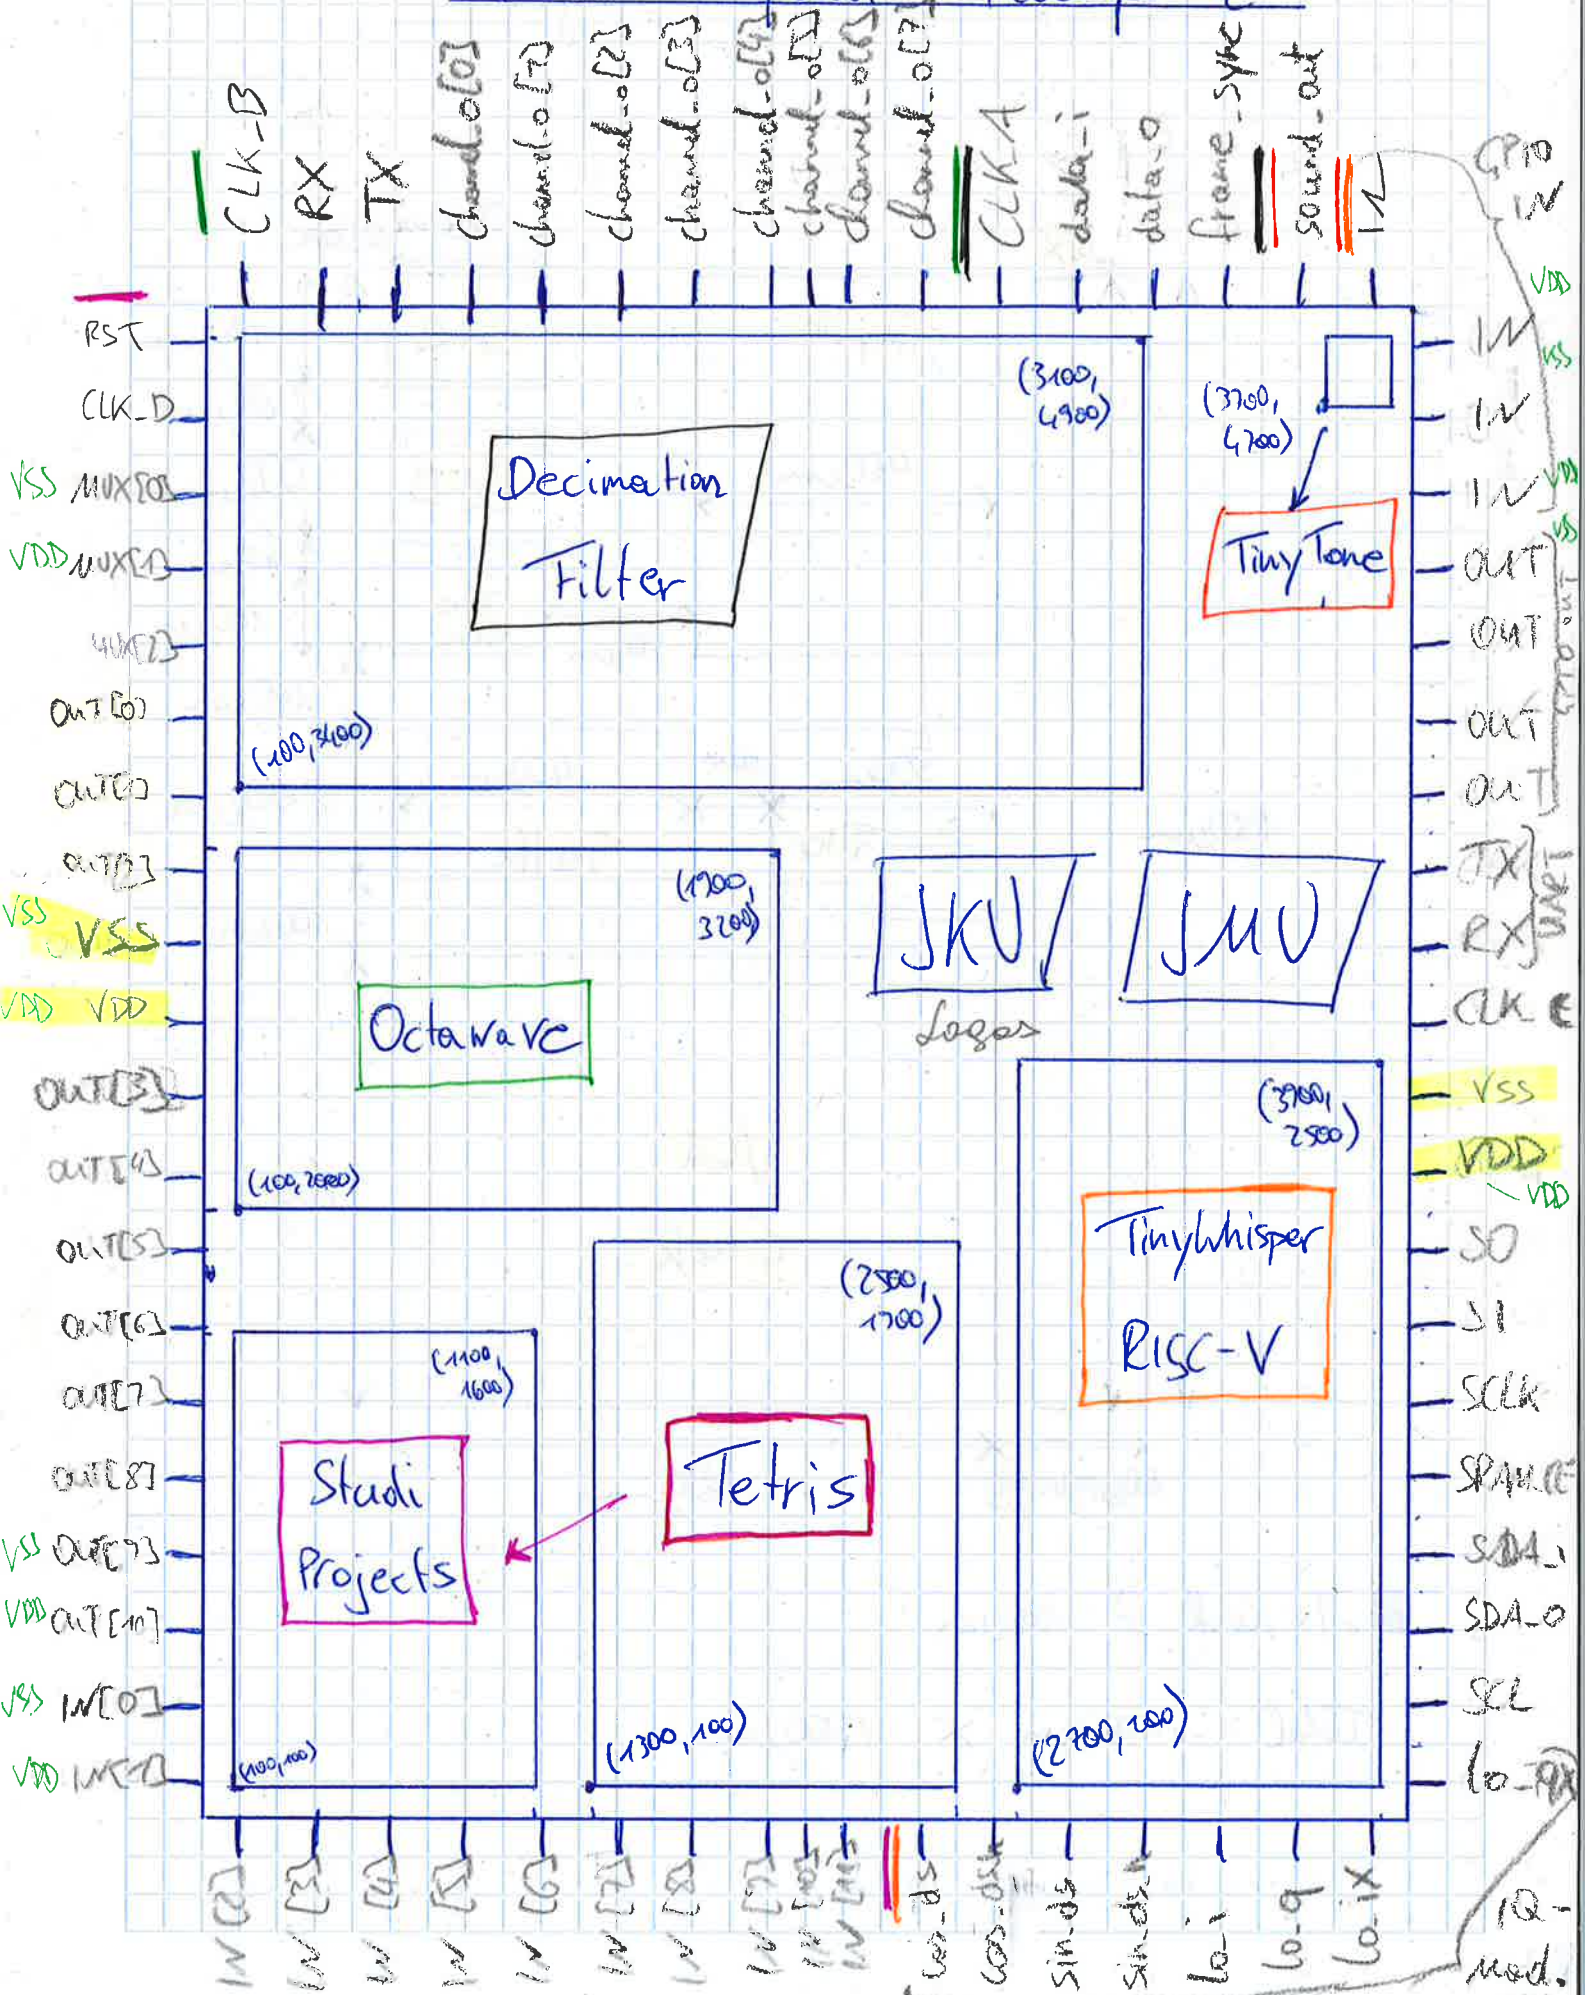

Floorplan - Student Projects

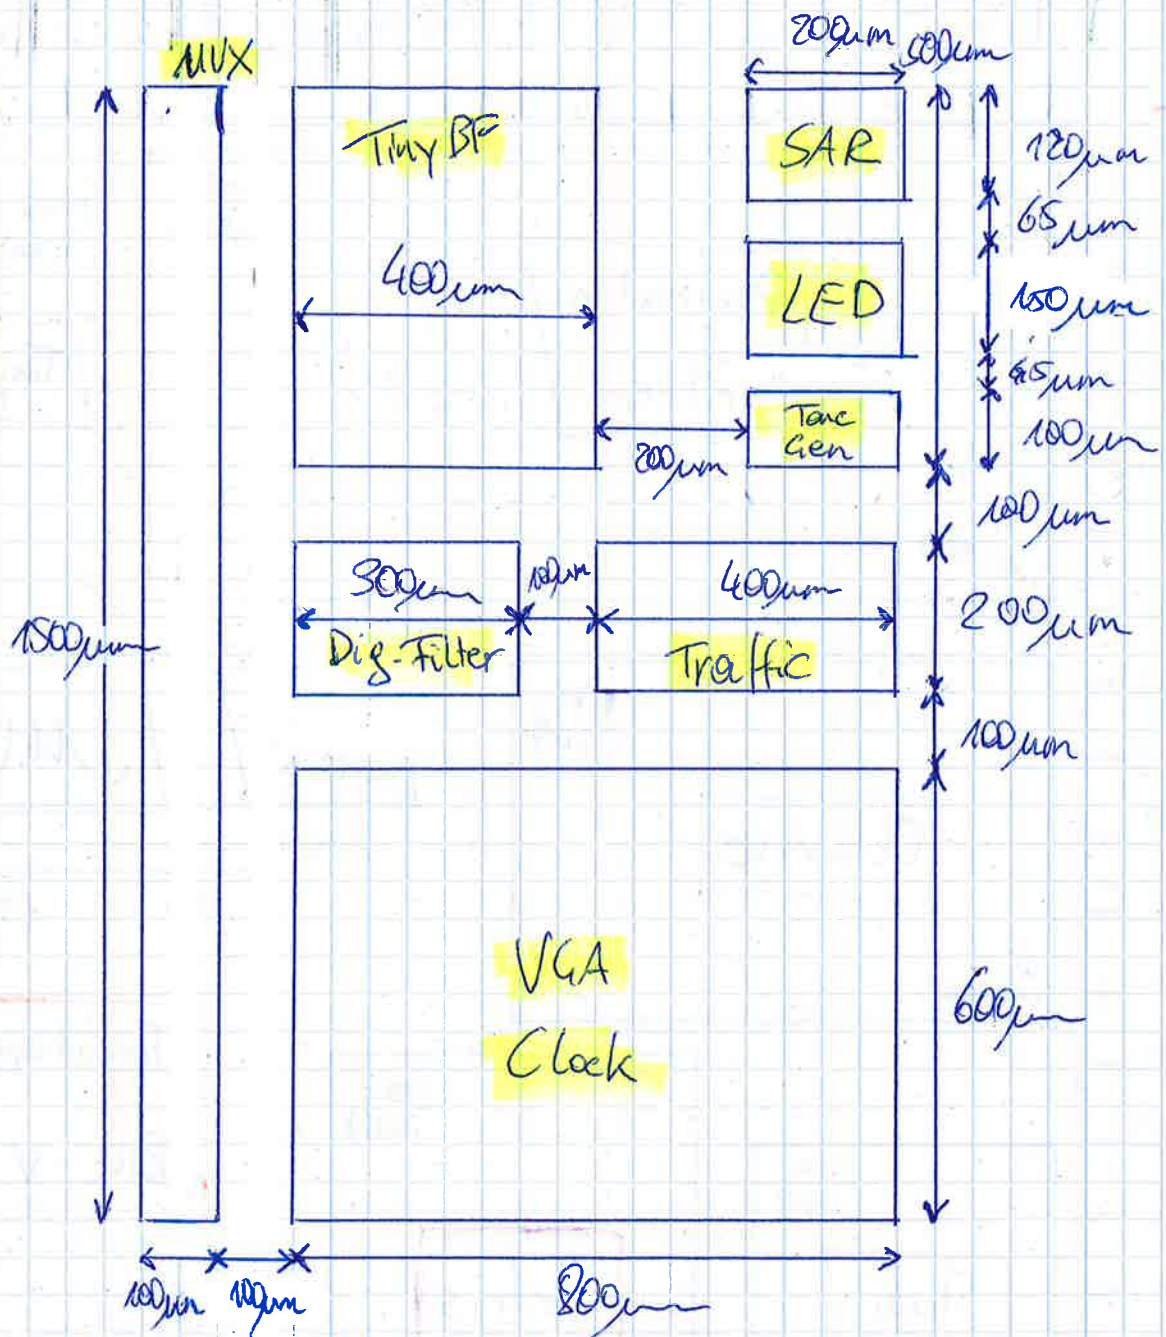

$2 \times \text{Kask} \geq 100\mu\text{m}$

Total: $1000\mu\text{m} \times 1500\mu\text{m}$