


1 Kcell $\approx$ 100 μ m

GF180 Tapeout Floorplan

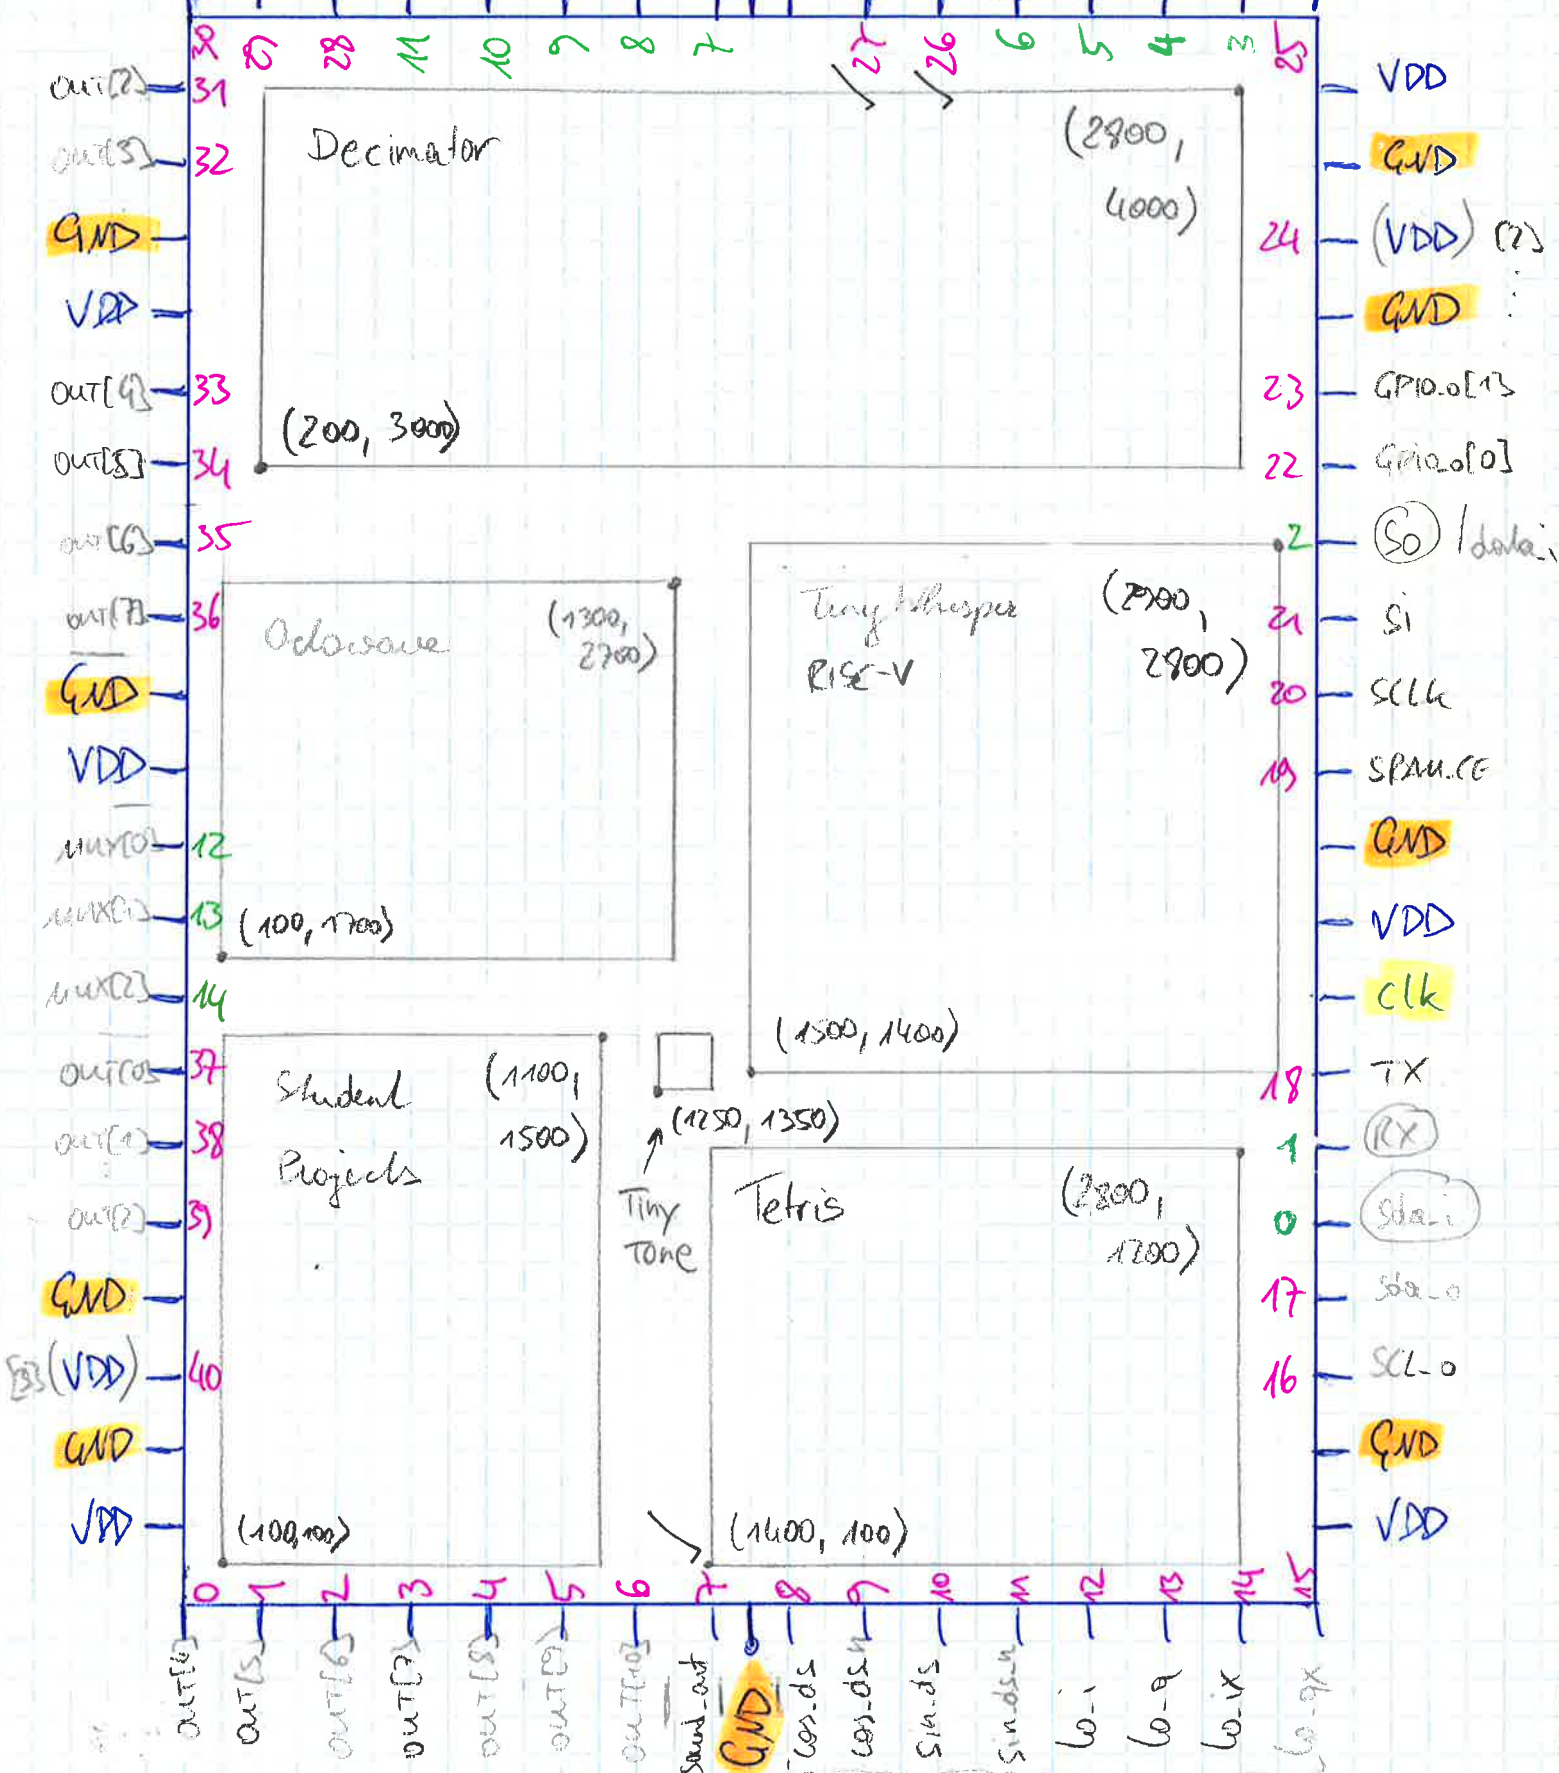


(466, 461)

$466 \approx 442 + 24$
 $461 \approx 442 + 19$

IO-Modulator

Floorplan - Student Projects

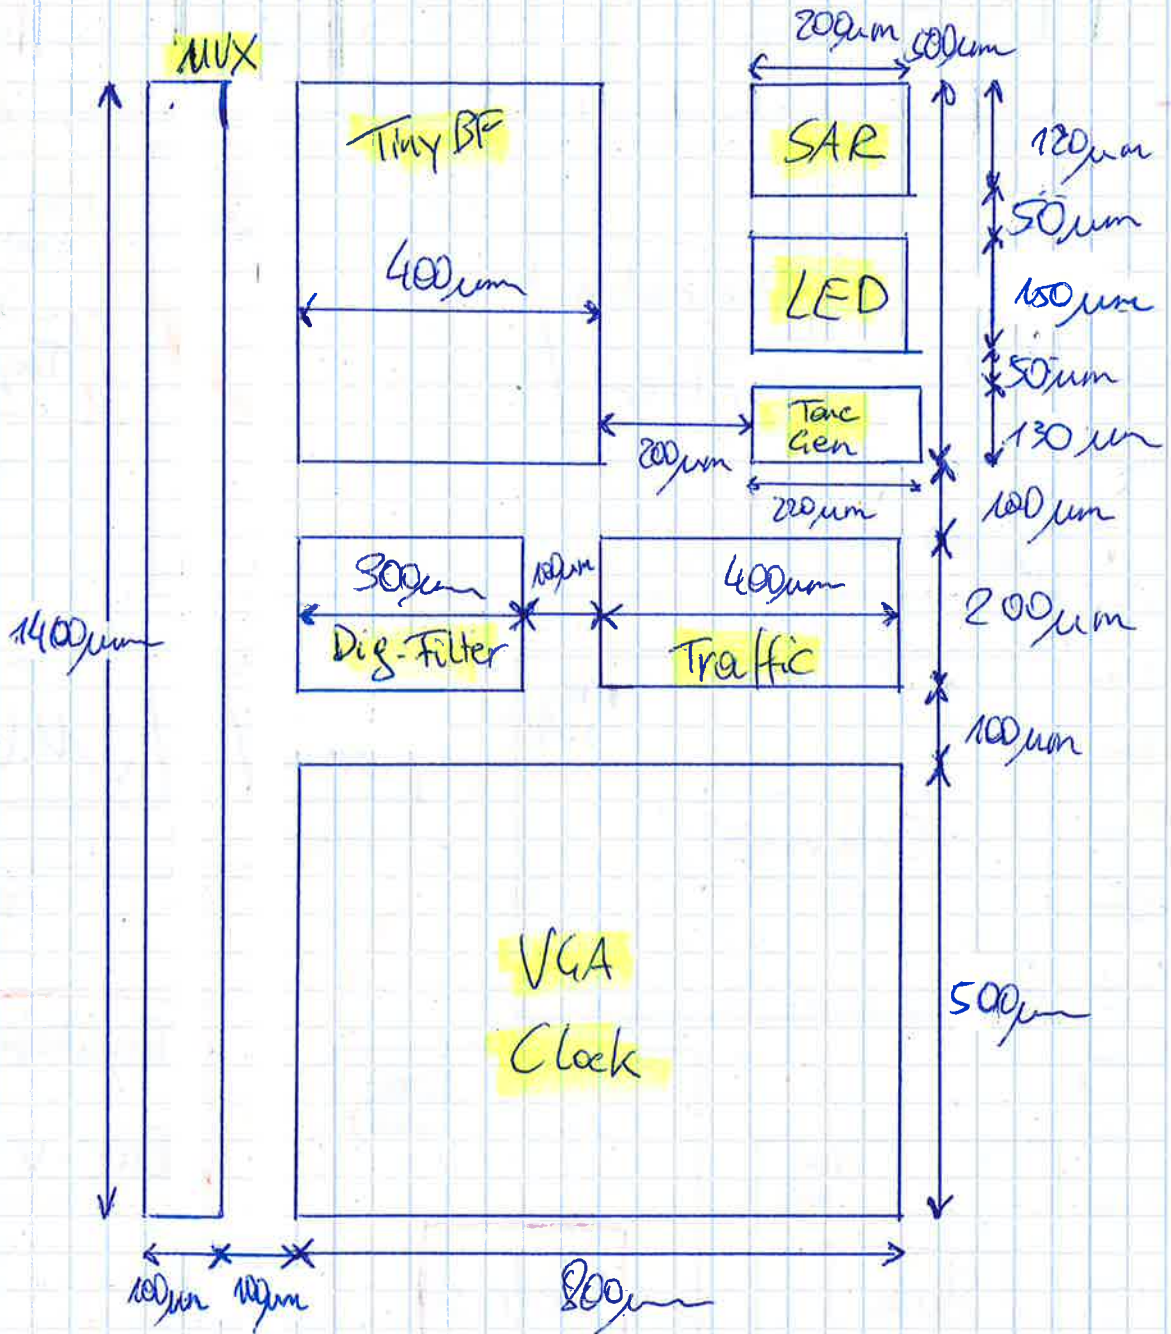

2 x 100 μm $\hat{=}$ 100 μm

Total: 1000 μm $\times$ 1400 μm