


1 Kcell $\approx$ 100 μ m

GF180 Tapeout Floorplan

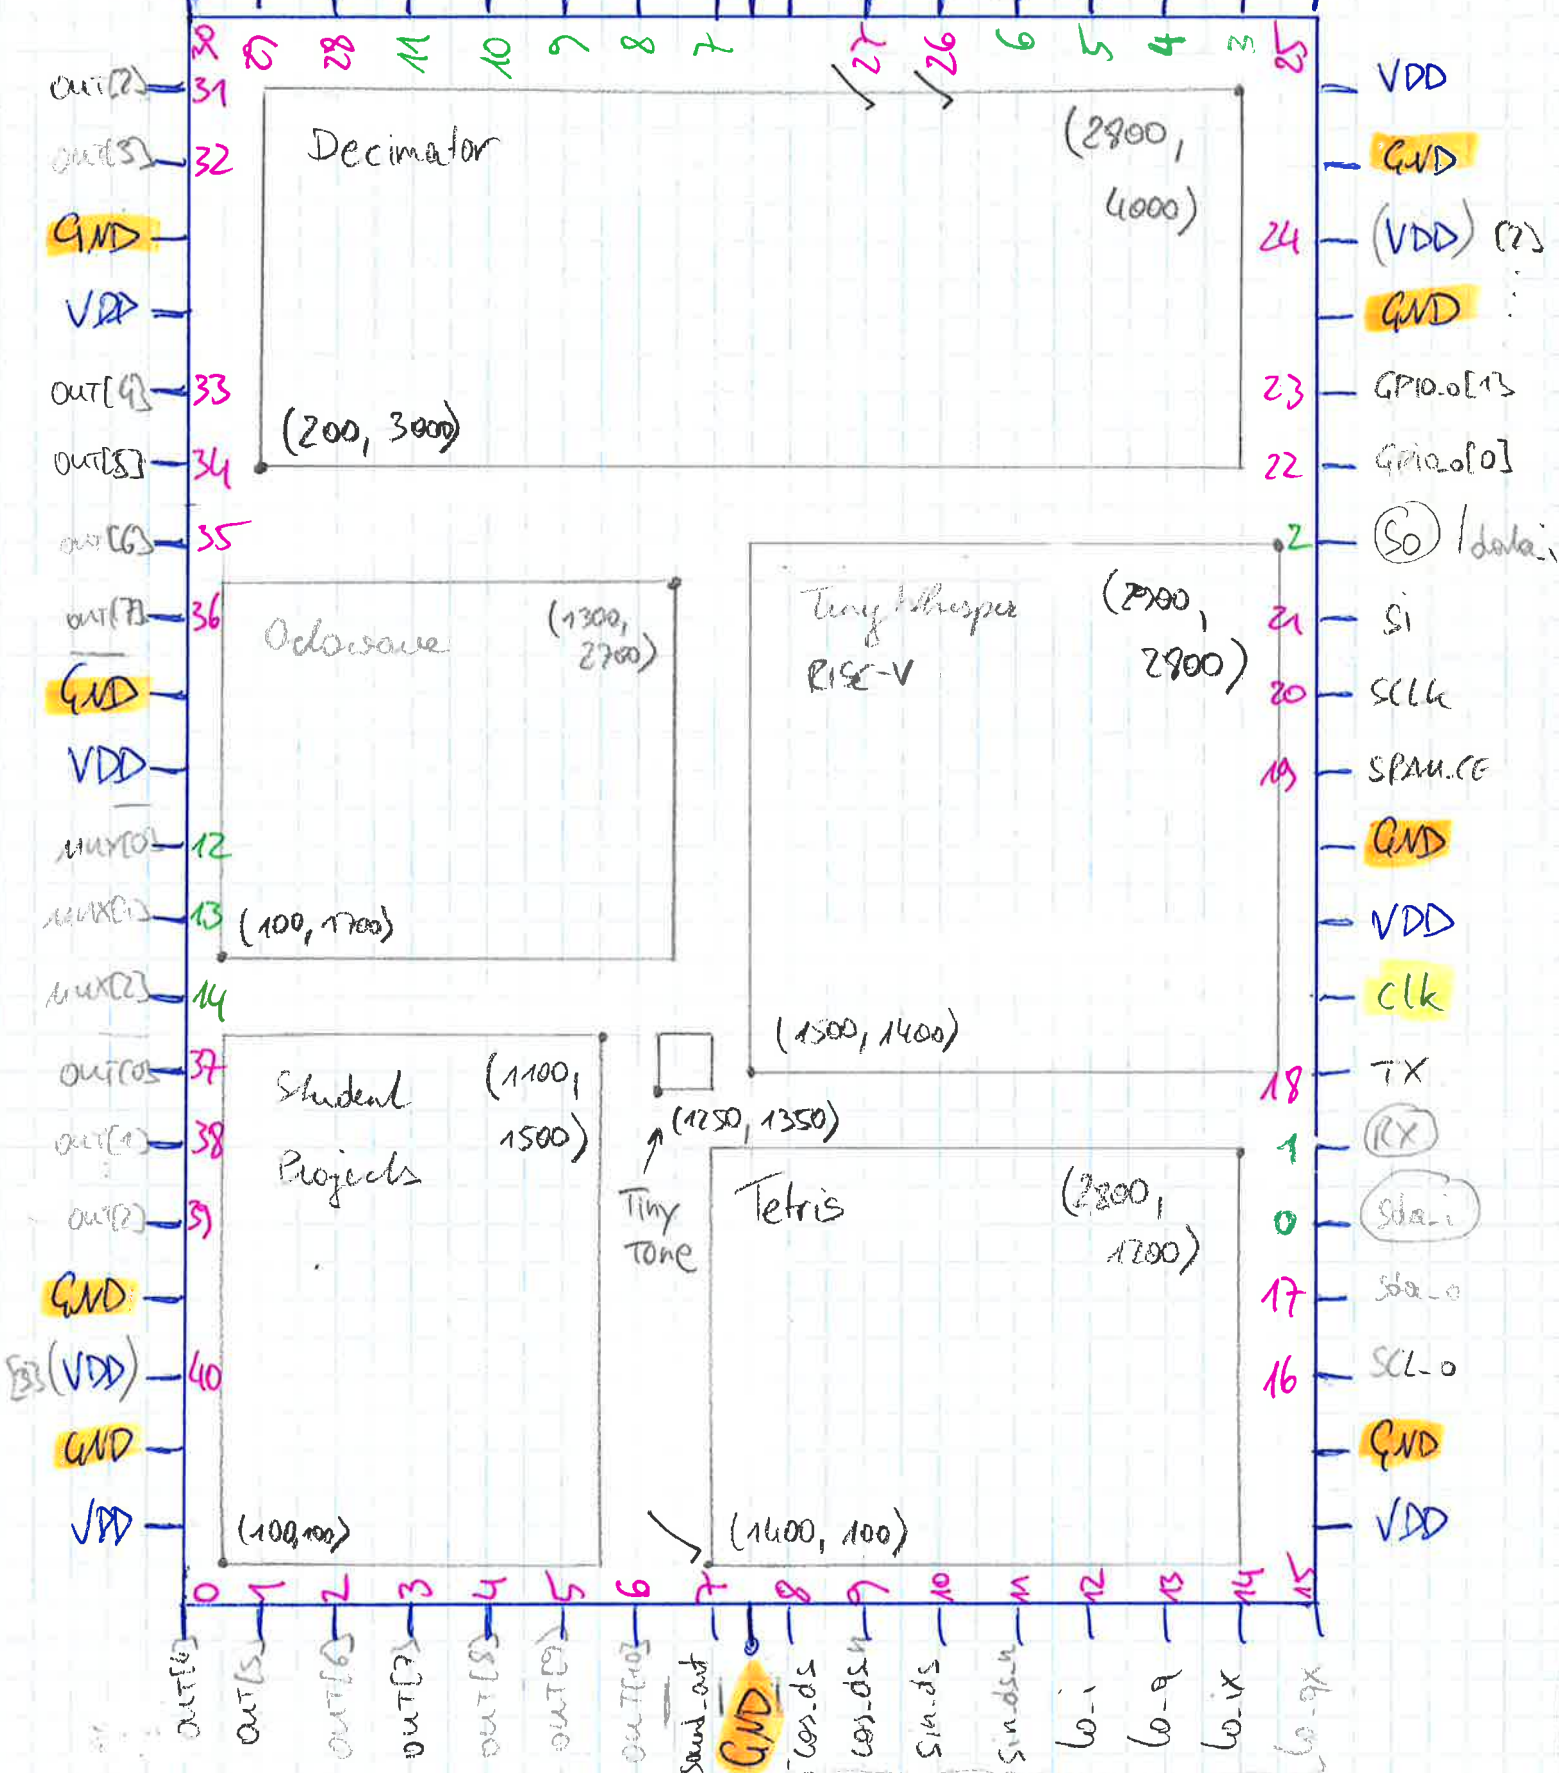


(466, 461)

$466 \approx 442 + 24$
 $461 \approx 442 + 19$

IO-Modulator

Floorplan - Student Projects

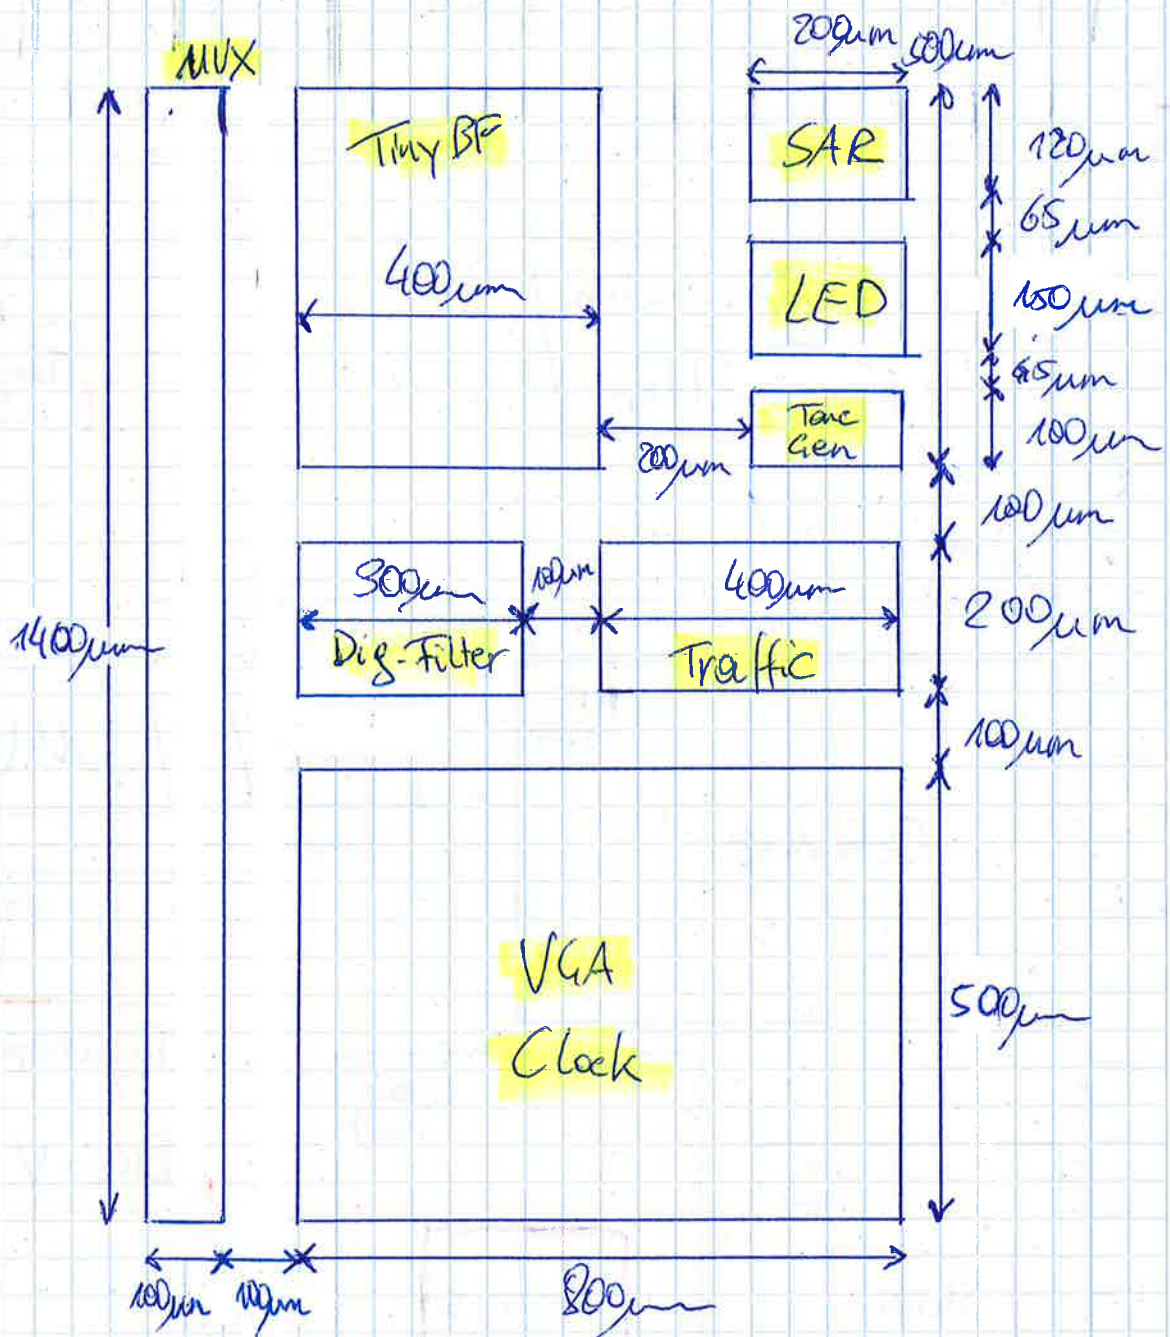

2 x 100µm ≥ 100µm

Total: 1000µm × 1400µm