


GF 180 Tapeout - Floorplan

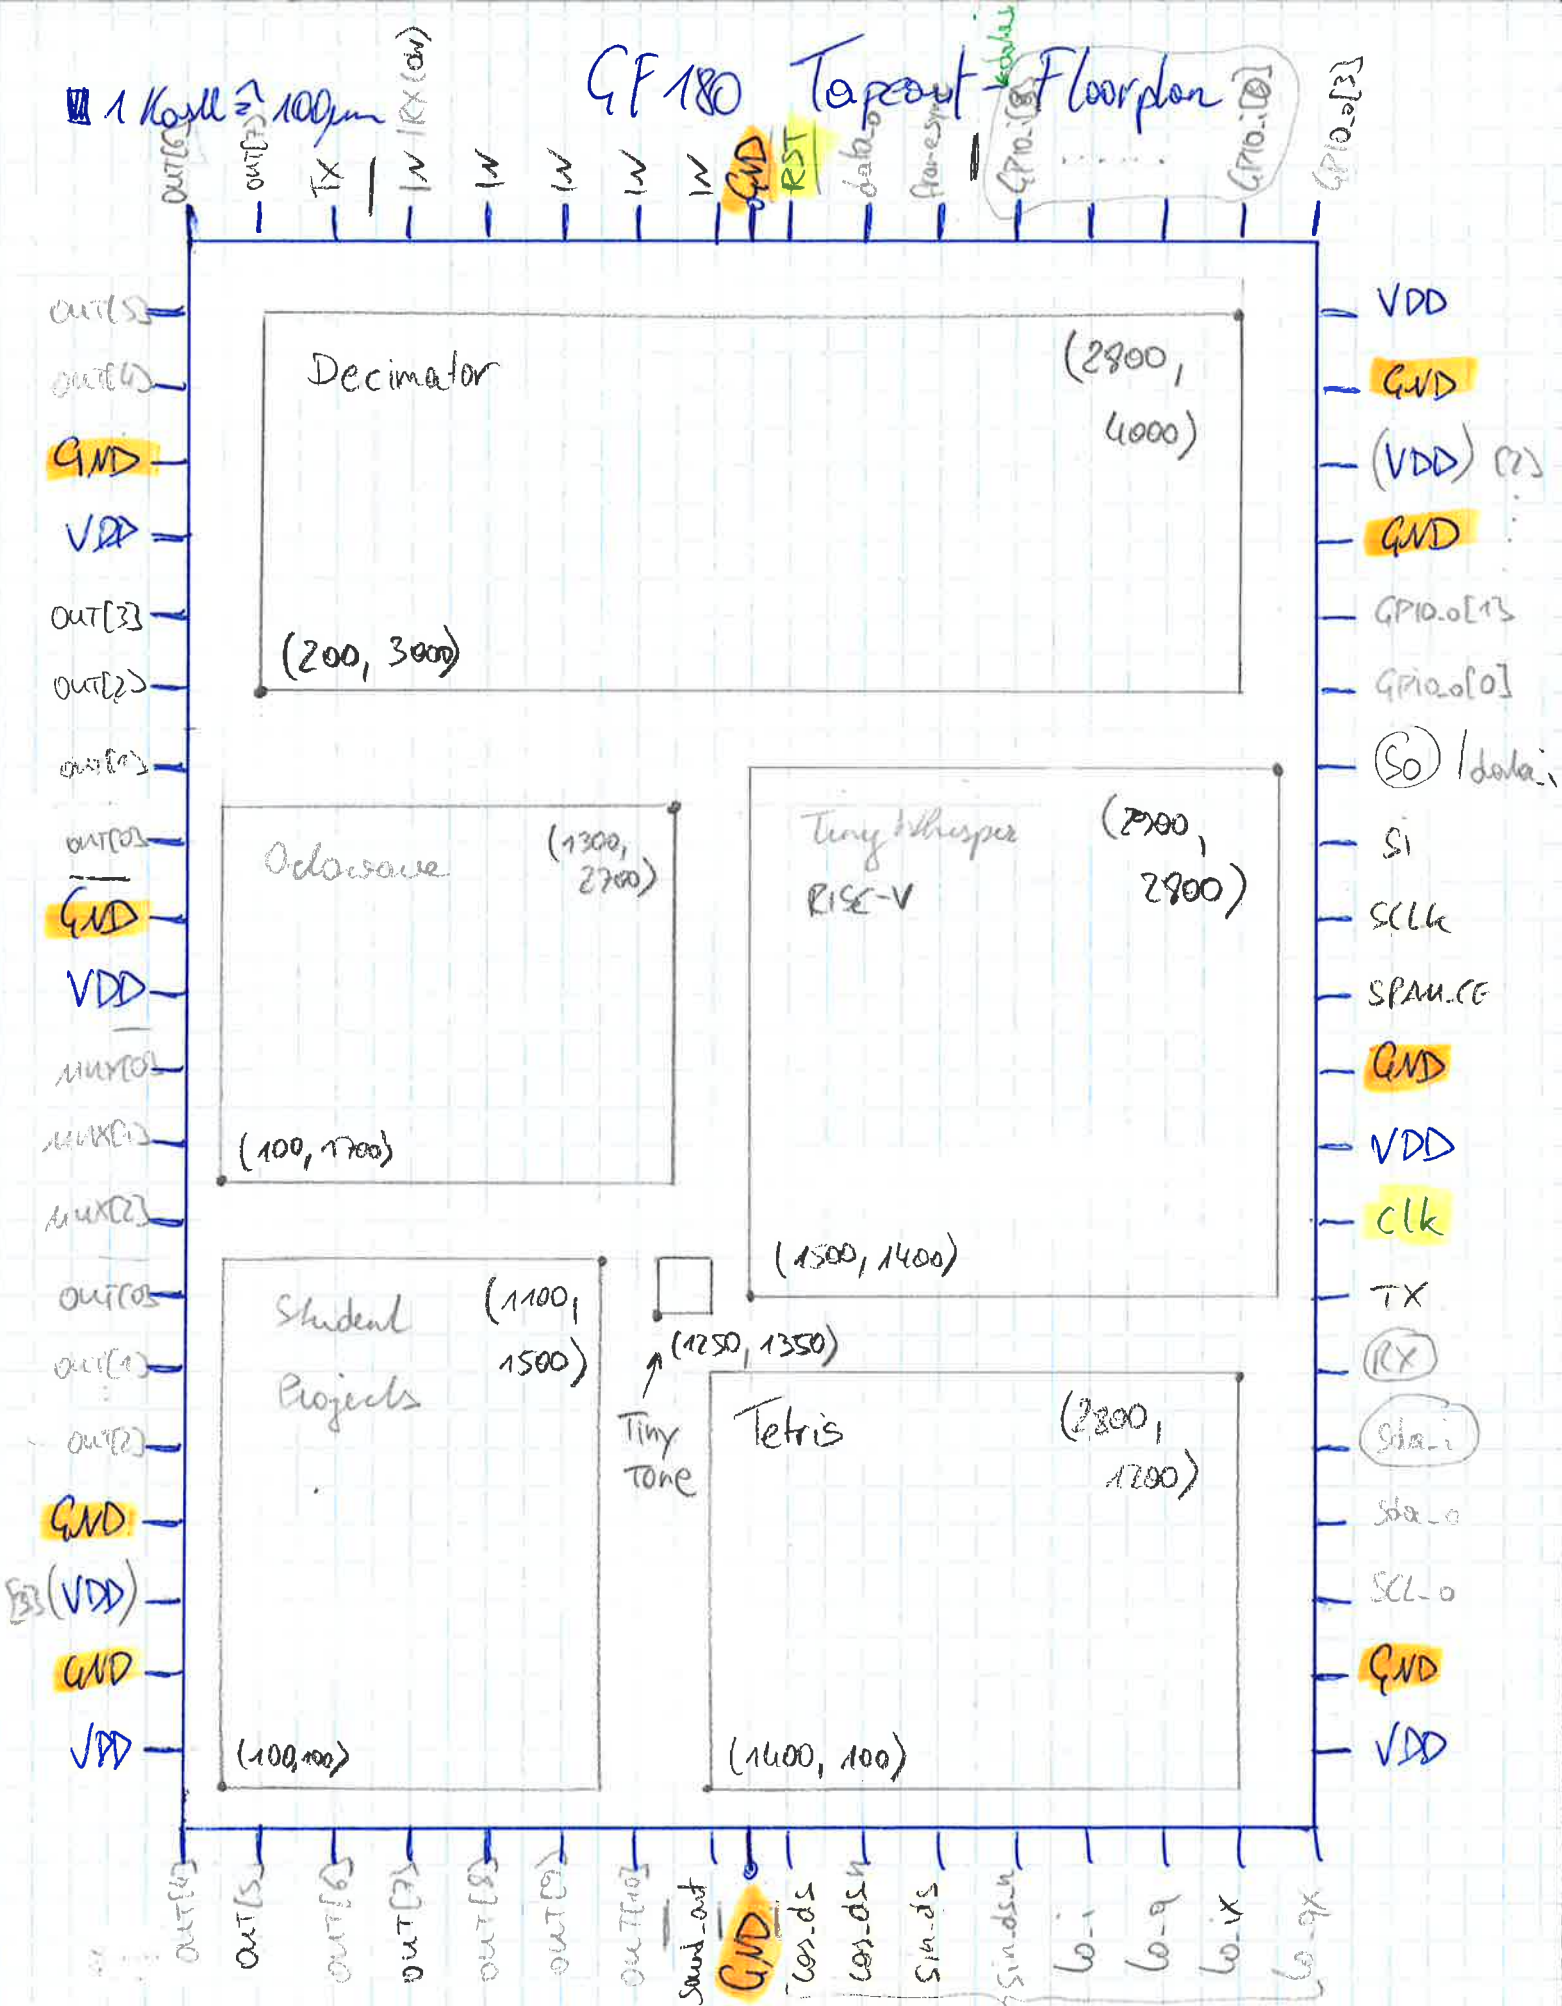


(466, 461)

$$466 = 442 + 24$$

$$461 = 442 + 19$$

Floorplan - Student Projects

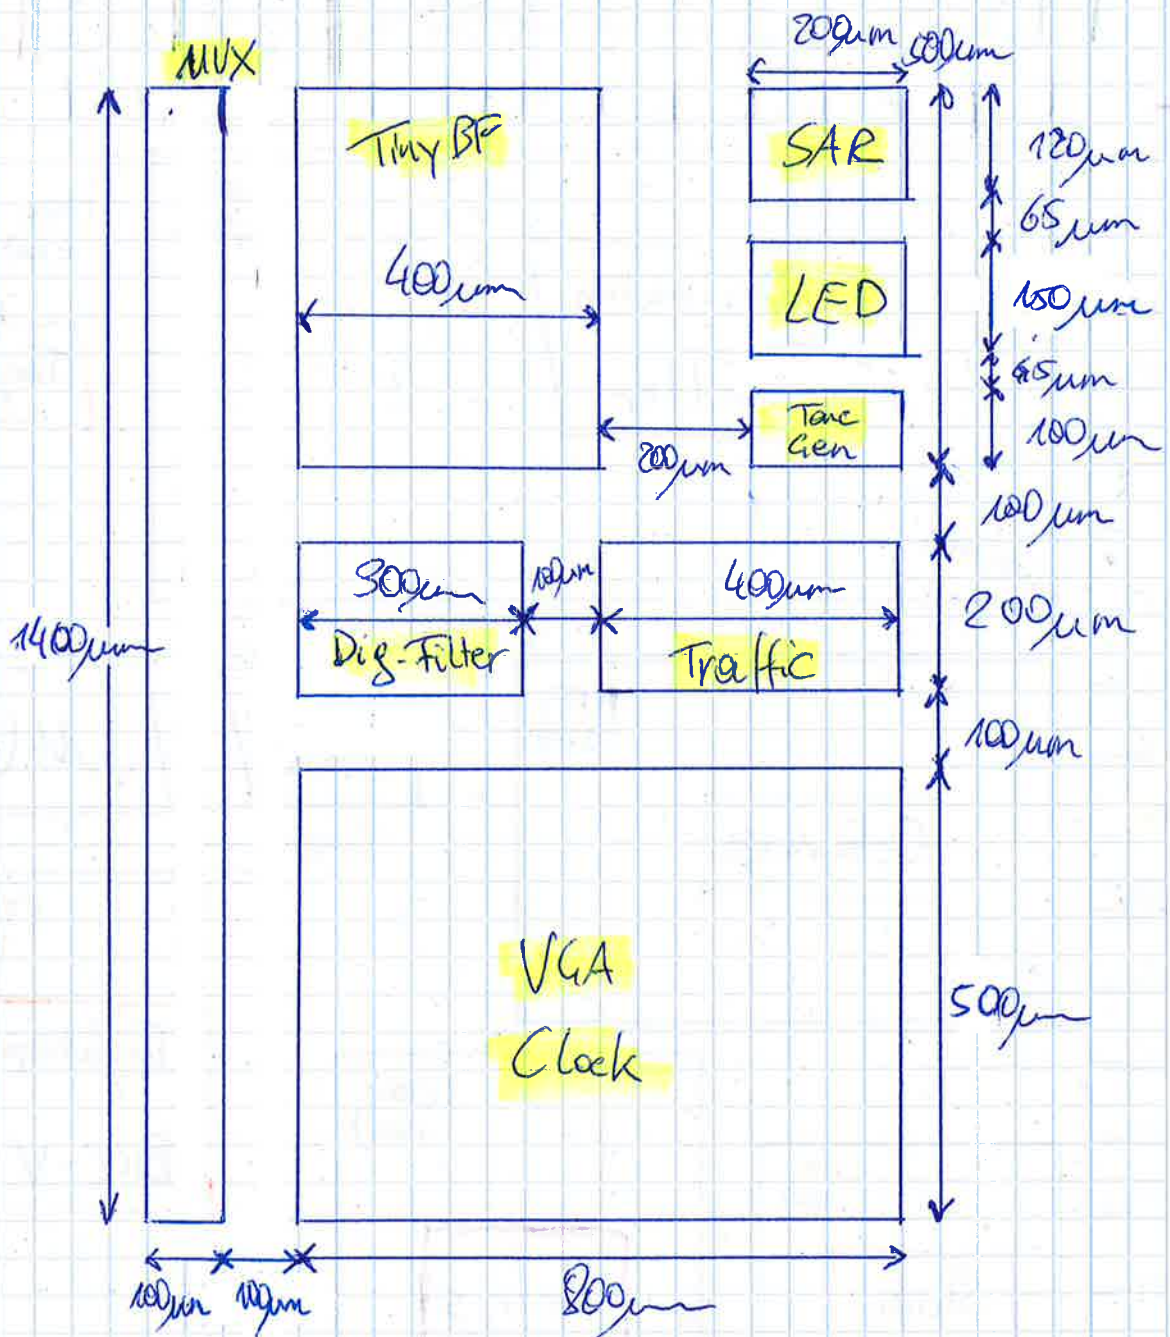

2 x 100µm ≥ 100µm

Total: 1000µm x 1400µm