



GF180 Tapeout - Floorplan

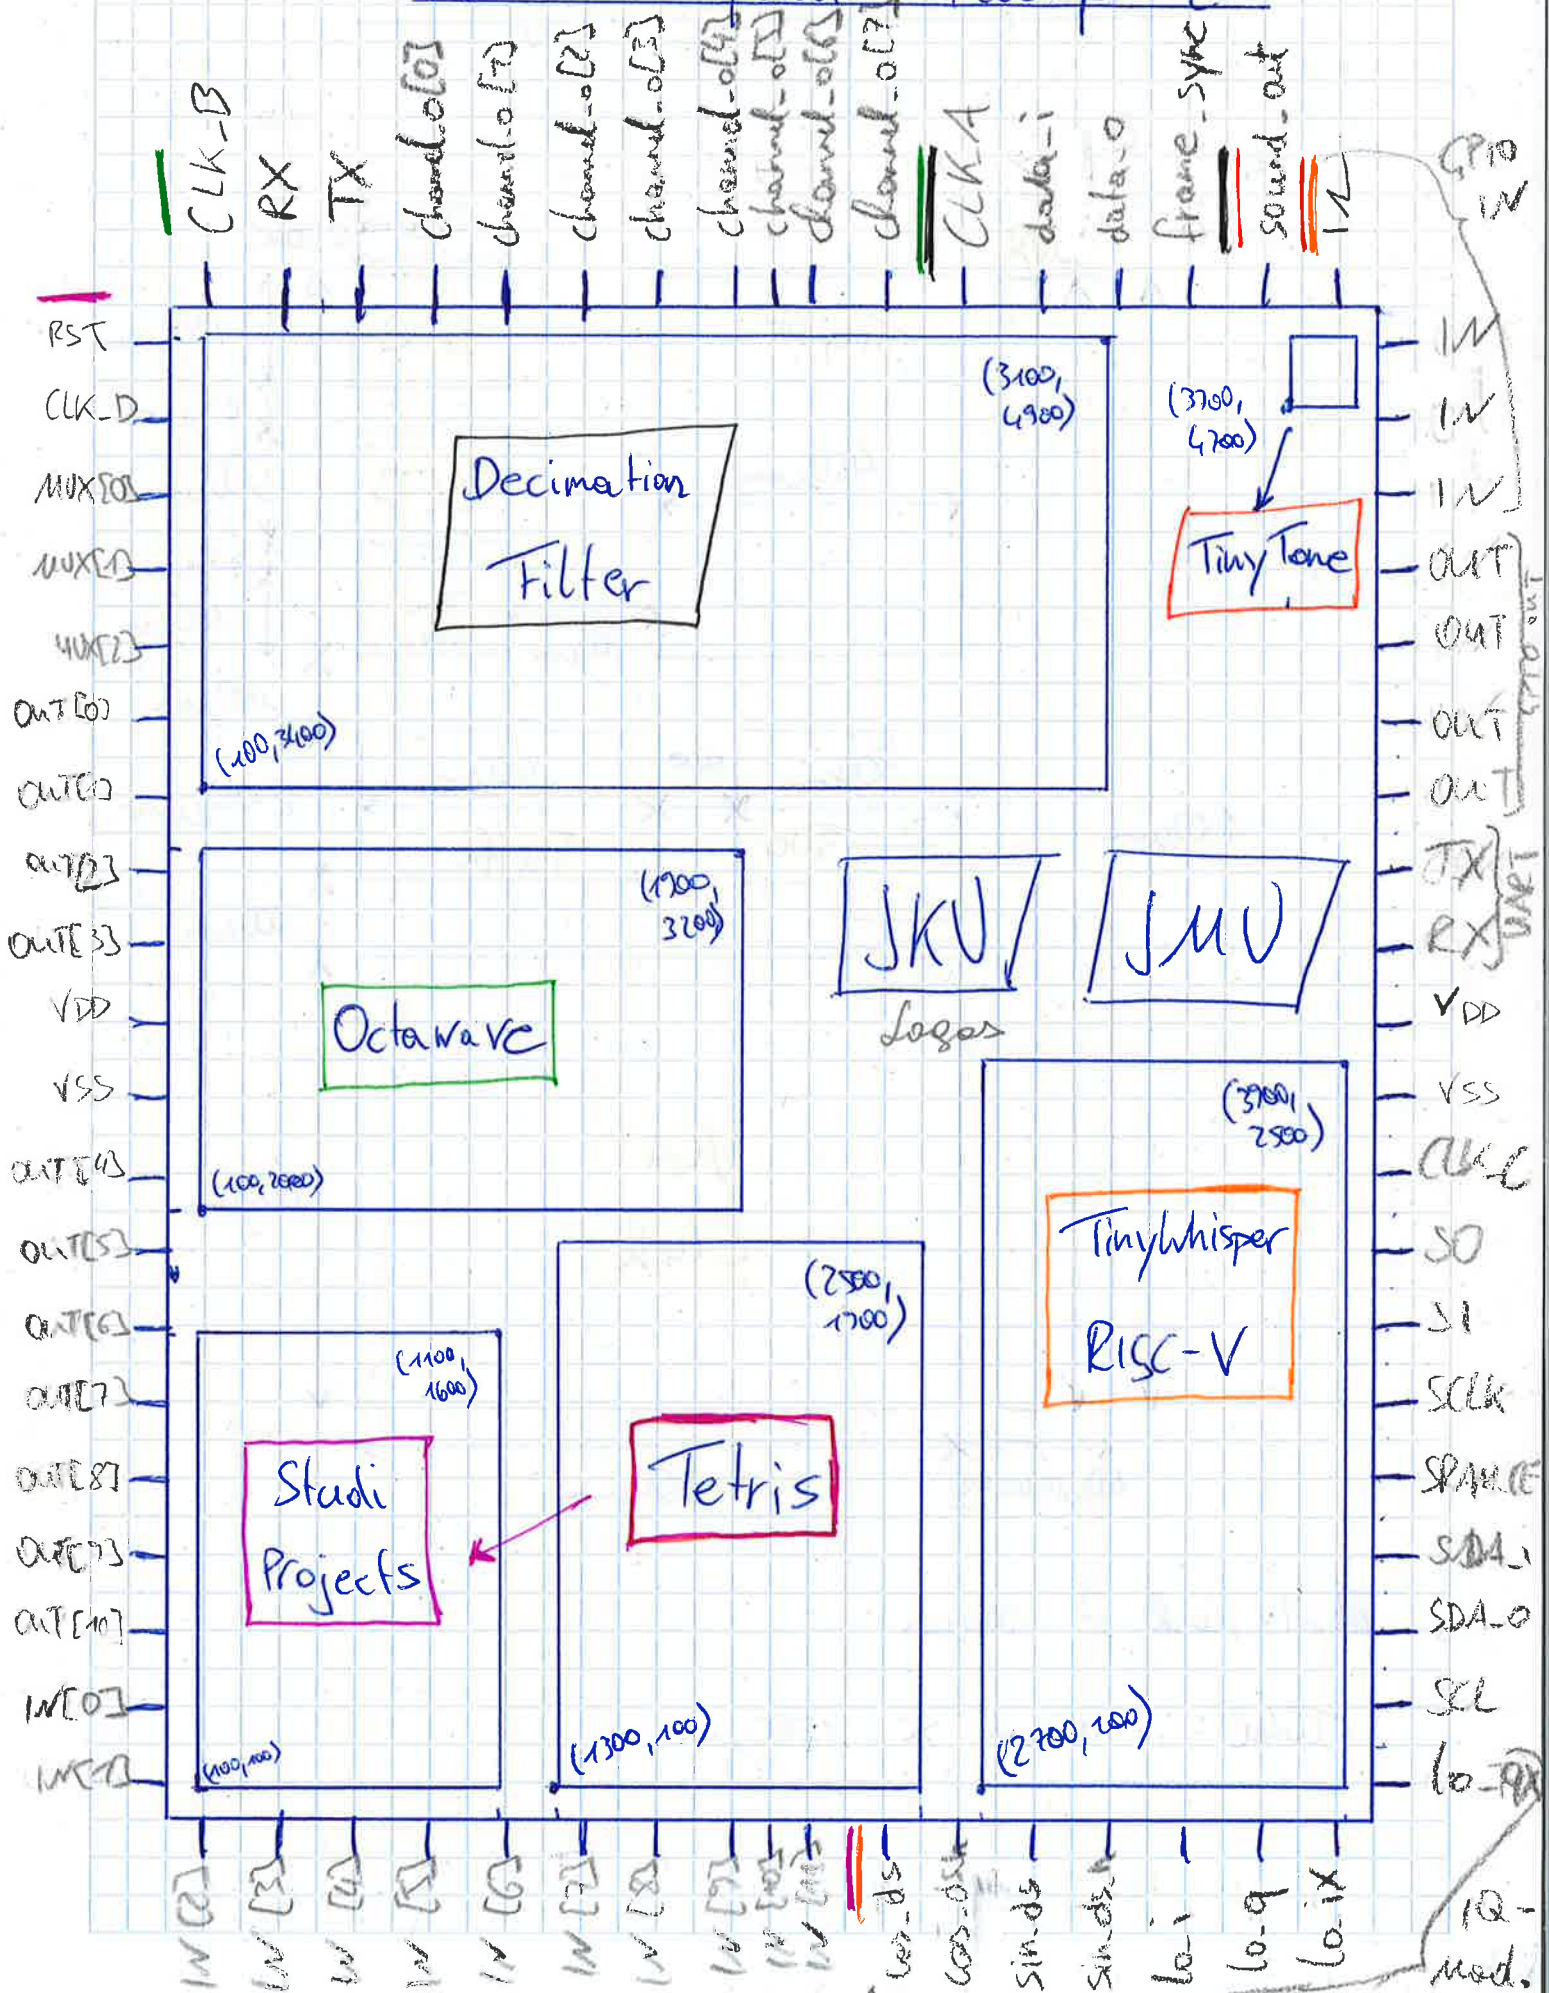

Floorplan - Student Projects

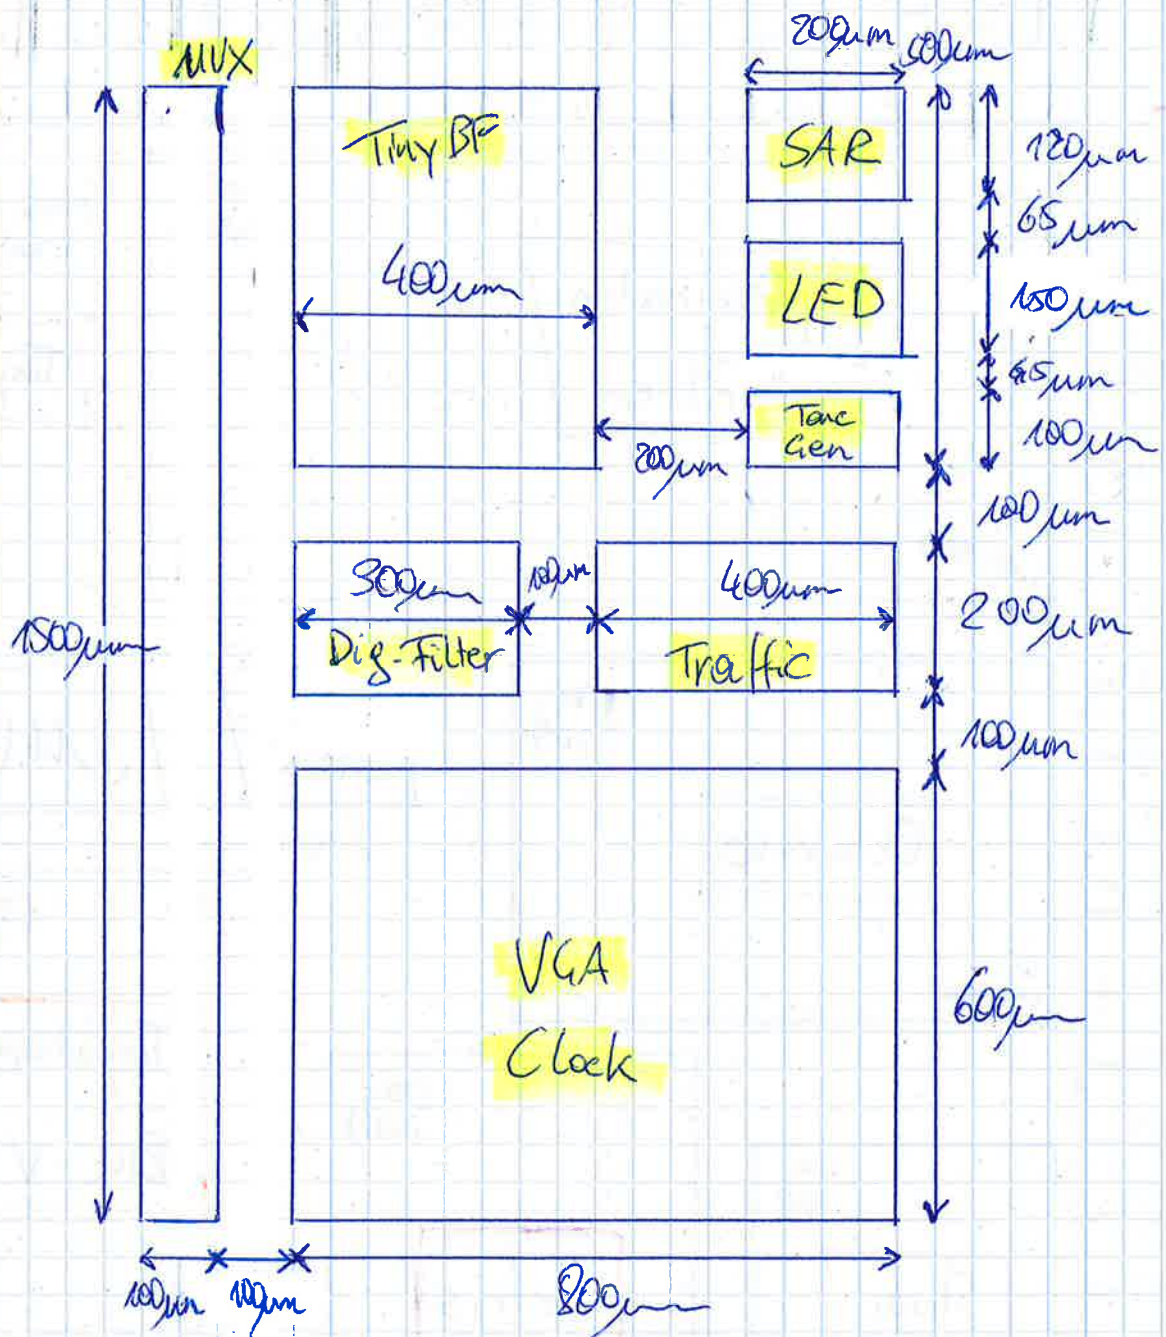

2 x 100µm ≥ 100µm

Total: 1000µm × 1500µm