



1 Kcell $\approx$ 100 μ m GF 18 μ i Tapeout - Floorplan

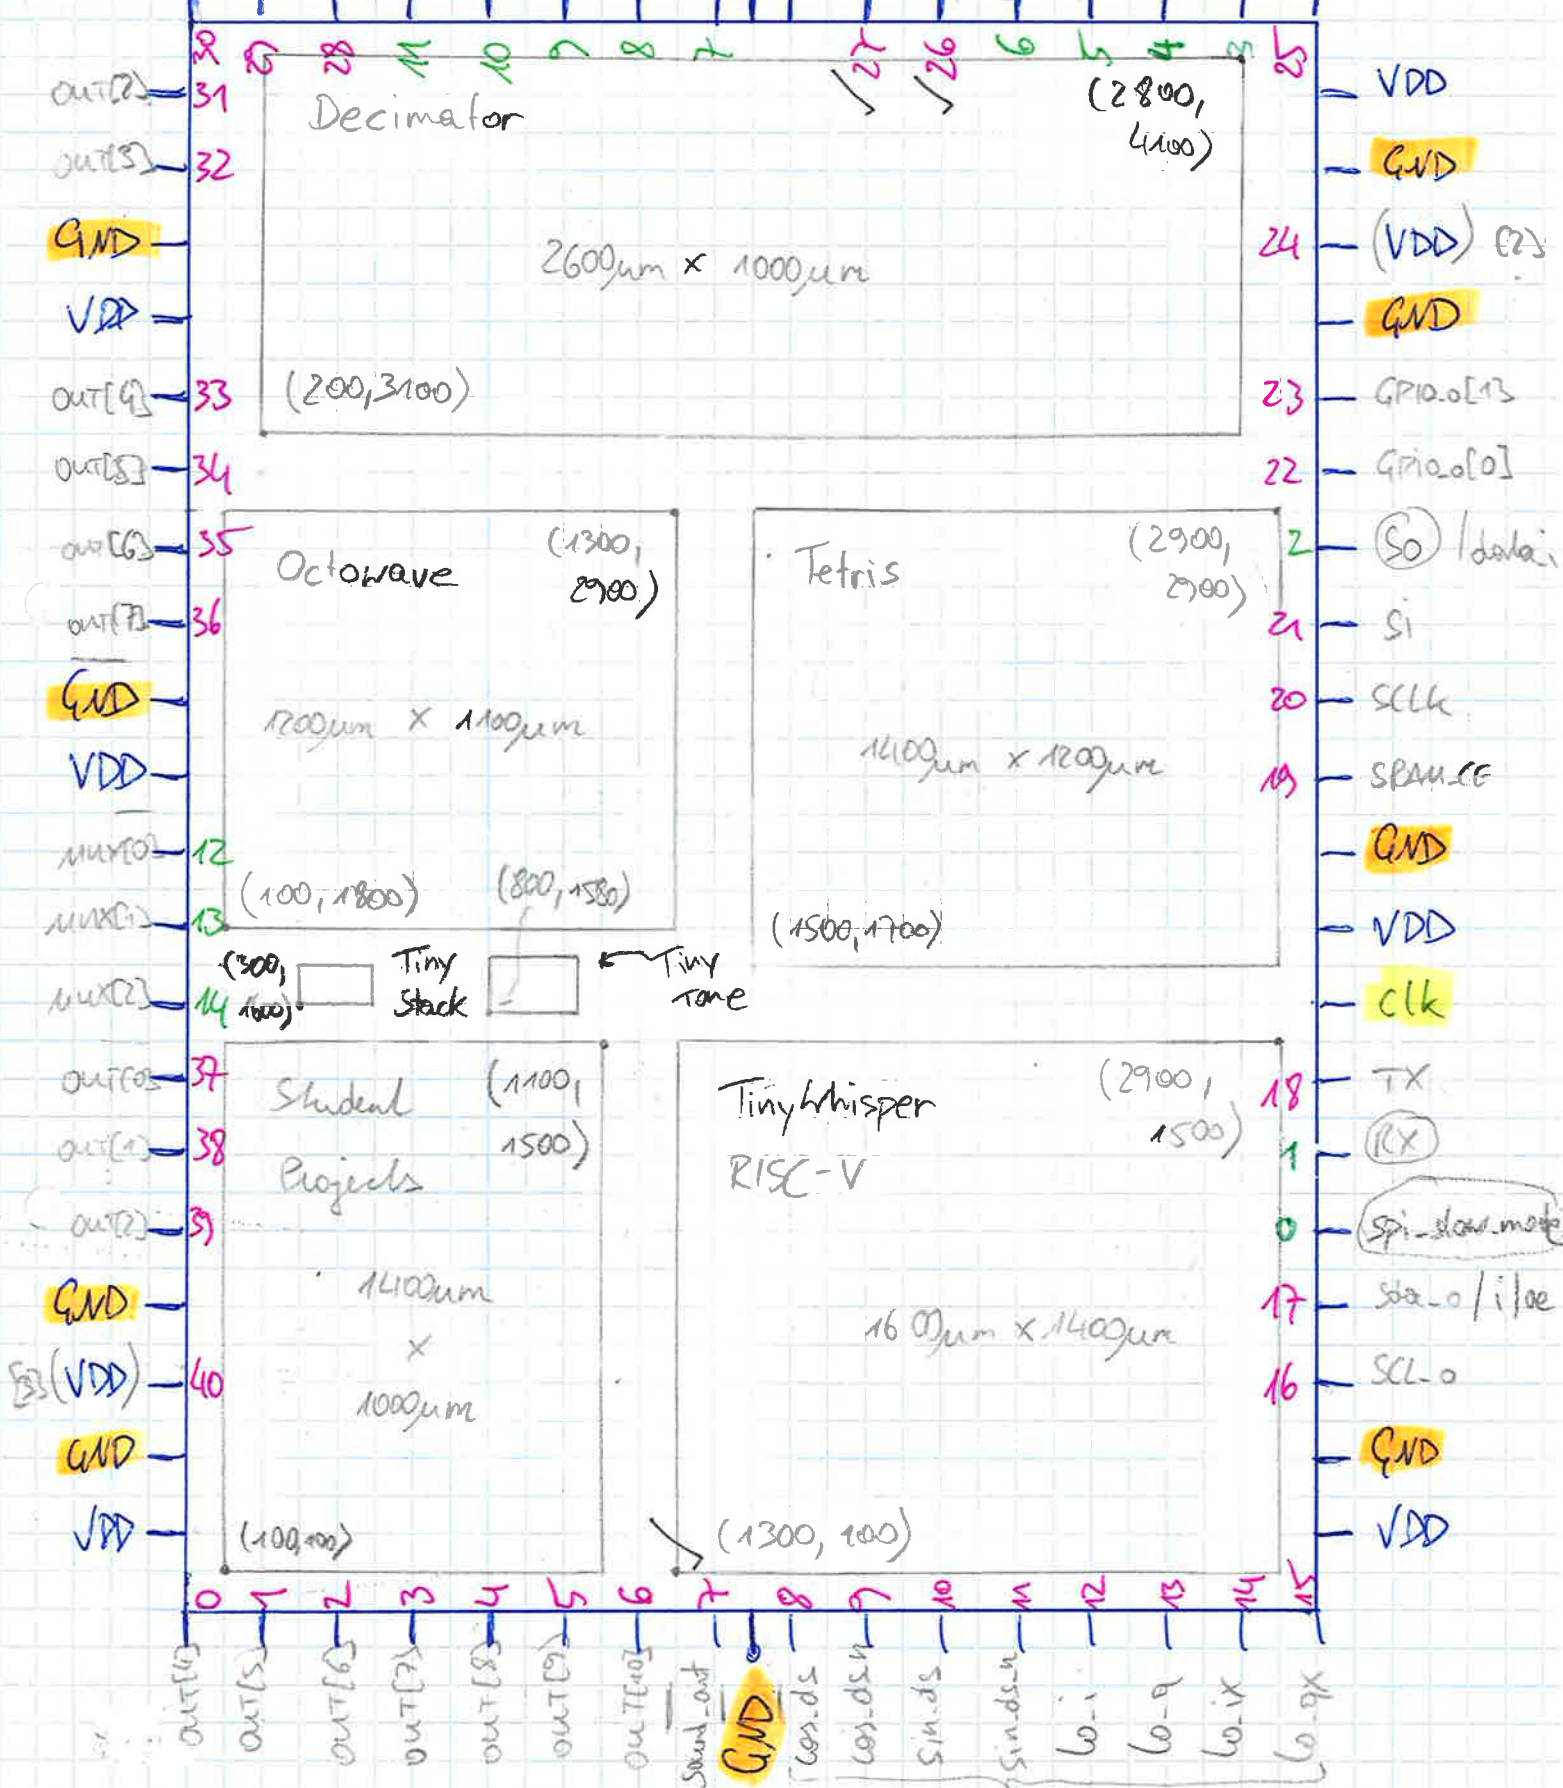

$466 = 442 + 24$
 $461 = 442 + 19$

Floorplan - Student Projects

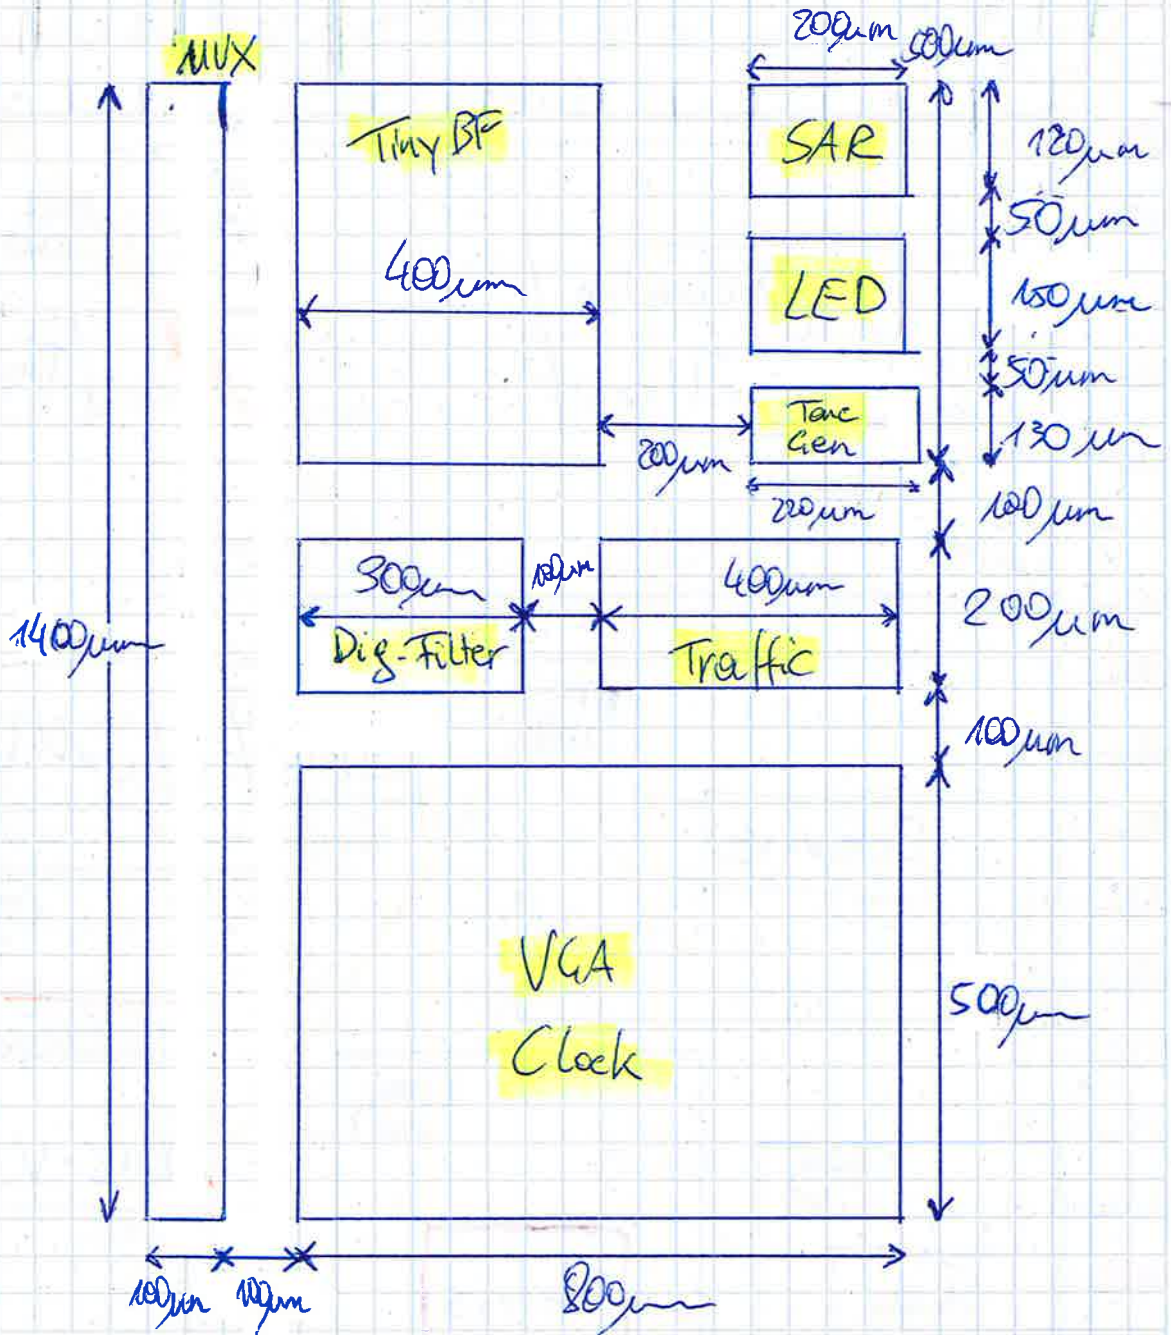

2 x Kask $\hat{=}$ 100µm

Total: 1000µm $\times$ 1400µm